

DOOR SCHEDULE

OPENING CODE	ROOM #	ROOM NAME	OPERATION	SIZE WxH RO	DESCRIPTION	VENDOR	MODEL	FINISH				HARDWARE			NOTES
								MATERIAL	GLAZING	INTERIOR	EXTERIOR	TYPE	MODEL	FINISH	
101	101	MASTER BEDROOM	SLIDING XO	8'-0" x 6'-8"	EXTERIOR TWO PANELS	MILGARD	SLIDING DOOR TWO PANEL	ALUMINUM	CLEAR	BRONZE	BRONZE	LOCKING	INCLUDED	BRONZE	(N) TO REPLACE (E)
102	102	MASTER BATHROOM	INSWING - SEE PLAN	2'-8" x 6'-8"	INTERIOR	TBD	TBD	SOLID CORE	NA	PAINT	PAINT	LOCKING	EMTEK	BLACK	(N) - SEE SPEC SCHEDULE FOR HANDLE SPEC
103	103	MASTER CLOSET	POCKET	2'-8" x 6'-8"	INTERIOR	TBD	TBD	SOLID CORE	NA	PAINT	PAINT	PASSAGE	EMTEK	BLACK	(N) - SEE SPEC SCHEDULE FOR HANDLE SPEC
104	104	LIVING ROOM	POCKET	3'-0 1/2" VIF x 8'-0"	INTERIOR TRIMLESS	TBD	TBD	SOLID CORE	NA	PAINT	PAINT	PASSAGE	EMTEK	BLACK	(N) - ADAPT SIZE TO HALLWAY OPENING
105	104	LIVING ROOM	SLIDING XO	6'-0" x 6'-8"	EXTERIOR TWO PANELS	MILGARD	SLIDING DOOR TWO PANEL	ALUMINUM	CLEAR	BRONZE	BRONZE	LOCKING	INCLUDED	BRONZE	(N) TO REPLACE (E)
106	104	LIVING ROOM	SLIDING OX	8'-0" x 6'-8"	EXTERIOR TWO PANELS	MILGARD	SLIDING DOOR TWO PANEL	ALUMINUM	CLEAR	BRONZE	BRONZE	LOCKING	INCLUDED	BRONZE	(N) AT (E) WINDOW LOCATION
107	104	LIVING ROOM	INSWING - SEE PLAN	3'-6" x 6'-8"	EXTERIOR ENTRY DOOR	SIMPSON	7002 DOUG FIR	CLEAR	STAINED WOOD	STAINED WOOD	STAINED WOOD	LOCKING	BALDWIN	BLACK	(N) TO REPLACE (E) - NO CHANGE TO SIZE - SEE SPECIFICATION SCHEDULE FOR HARDWARE
108	106	LAUNDRY	POCKET	3'-0" x 6'-8"	INTERIOR	TBD	TBD	SOLID CORE	NA	PAINT	PAINT	PASSAGE	EMTEK	BLACK	(N) - SEE SPEC SCHEDULE FOR HANDLE SPEC
109	107	POWDER ROOM	POCKET	3'-0" x 6'-8"	INTERIOR	TBD	TBD	SOLID CORE	NA	PAINT	PAINT	LOCKING	EMTEK	BLACK	(N)
110	105	KITCHEN	SLIDING OX	8'-0" x 6'-8"	EXTERIOR TWO PANELS	MILGARD	SLIDING DOOR TWO PANEL	ALUMINUM	CLEAR	BRONZE	BRONZE	LOCKING	INCLUDED	BRONZE	(N)
111	110	BEDROOM	MIRROR POCKET	4'-1" VIF x 6'-8"	INTERIOR TWO PANELS	TBD	TBD	SOLID CORE	NA	PAINT	PAINT	PASSAGE	TBD	TBD	(N)
112	109	BATHROOM	MIRROR POCKET	2'-6" x 6'-8"	INTERIOR TWO PANELS	TBD	TBD	SOLID CORE	NA	PAINT	PAINT	LOCKING	TBD	TBD	(N)
113	110	BEDROOM	SLIDING OX	8'-0" x 6'-8"	EXTERIOR TWO PANELS	MILGARD	SLIDING DOOR TWO PANEL	ALUMINUM	CLEAR	BRONZE	BRONZE	LOCKING	INCLUDED	BRONZE	(N) TO REPLACE (E)
114	103	MASTER CLOSET	SLIDING XXX OR XXO	6'-2 1/2" VIF x 8'-0"	INTERIOR THREE PANELS CLOSET DOOR	TBD	TBD	SOLID CORE	NA	PAINT	PAINT	LOCKING	TBD	TBD	(N)
115	110	BEDROOM	DOUBLE INTERIOR - SEE PLAN	2'-6" VIF x 8'-0"	INTERIOR DOUBLE CLOSET DOOR	TBD	TBD	SOLID CORE	NA	PAINT	PAINT	PASSAGE	EMTEK	BLACK	(N) - SEE SPEC SCHEDULE FOR HANDLE SPEC

WINDOW SCHEDULE

OPENING CODE	ROOM #	ROOM NAME	OPERATION	SIZE WxH RO	VENDOR	MODEL	FINISH				HARDWARE			NOTES
							MATERIAL	GLAZING	INTERIOR	EXTERIOR	TYPE	MODEL	FINISH	
A1	101	MASTER BEDROOM	FIXED	3'-10" x 5'-10"	MILGARD	PICTURE	ALUMINUM	CLEAR	BRONZE	BRONZE	NA	NA	NA	(N)
A2	101	MASTER BEDROOM	FIXED	3'-10" x 5'-10"	MILGARD	PICTURE	ALUMINUM	CLEAR	BRONZE	BRONZE	NA	NA	NA	(N) TO REPLACE (E) - NO CHANGE TO SIZE
A3	101	MASTER BEDROOM	DOUBLE AWNING BELOW PICTURE	5'-10" x 5'-10"	MILGARD	AWNING TWO WIDE BELOW PICTURE	ALUMINUM	CLEAR	BRONZE	BRONZE	LOCKING	CRANK	BRONZE	(N) TO REPLACE (E) - NO CHANGE TO SIZE
A4	102	MASTER BATHROOM	HORIZONTAL SLIDER XO	3'-10" x 1'-10"	MILGARD	HALF VENT	ALUMINUM	CLEAR	BRONZE	BRONZE	LOCKING	INCLUDED	BRONZE	(N) AT (E) WINDOW LOCATION - ELEVATED SILL
A5	103	MASTER CLOSET	FIXED	2'-0" x 5'-10"	MILGARD	PICTURE	ALUMINUM	CLEAR	BRONZE	BRONZE	NA	NA	NA	(N) AT (E) DOOR LOCATION
A6	104	LIVING ROOM	FIXED	2'-9" x 5'-10"	MILGARD	PICTURE	ALUMINUM	CLEAR	BRONZE	BRONZE	NA	NA	NA	(N) TO REPLACE (E) - LOWERED SILL
A7	104	LIVING ROOM	FIXED	2'-9" x 5'-10"	MILGARD	PICTURE	ALUMINUM	CLEAR	BRONZE	BRONZE	NA	NA	NA	(N) TO REPLACE (E) - LOWERED SILL
A8	105	KITCHEN	HORIZONTAL SLIDER XO	5'-11" x 3'-1"	MILGARD	HALF VENT	ALUMINUM	CLEAR	BRONZE	BRONZE	LOCKING	INCLUDED	BRONZE	(N) AT (E) DOOR LOCATION - ELEVATED SILL
A9	104	LIVING ROOM	FIXED	3'-10" x 5'-10"	MILGARD	PICTURE	ALUMINUM	CLEAR	BRONZE	BRONZE	NA	NA	NA	(N) TO REPLACE (E) - NO CHANGE TO SIZE
A10	104	LIVING ROOM	FIXED	4'-10" x 5'-10"	MILGARD	PICTURE	ALUMINUM	CLEAR	BRONZE	BRONZE	NA	NA	NA	(N) TO REPLACE (E) - NO CHANGE TO SIZE
A11	107	POWDER ROOM	HORIZONTAL SLIDER OX	2'-10" x 2'-10"	MILGARD	HALF VENT	ALUMINUM	CLEAR	BRONZE	BRONZE	LOCKING	INCLUDED	BRONZE	(N) TO REPLACE (E) - NO CHANGE TO SIZE
A12	108	HALLWAY	HORIZONTAL SLIDER XO	3'-10" x 3'-11"	MILGARD	HALF VENT	ALUMINUM	CLEAR	BRONZE	BRONZE	LOCKING	INCLUDED	BRONZE	(N) TO REPLACE (E) - NO CHANGE TO SIZE
A13	108	HALLWAY	FIXED	8'-4" x 3'-8"	MILGARD	PICTURE	ALUMINUM	CLEAR	BRONZE	BRONZE	NA	NA	NA	(N)
A14	110	BEDROOM	FIXED	2'-9" x 3'-8"	MILGARD	PICTURE	ALUMINUM	CLEAR	BRONZE	BRONZE	NA	NA	NA	(N)
A15	109	BATHROOM	HORIZONTAL SLIDER XO	3'-8" x 1'-10"	MILGARD	HALF VENT	ALUMINUM	CLEAR	BRONZE	BRONZE	LOCKING	CRANK	BRONZE	(N)
A16	110	BEDROOM	DOUBLE AWNING BELOW PICTURE	7'-10" x 5'-10"	MILGARD	AWNING TWO WIDE BELOW PICTURE	ALUMINUM	CLEAR	BRONZE	BRONZE	LOCKING	CRANK	BRONZE	(N) TO REPLACE (E) - NO CHANGE TO SIZE

GENERAL NOTES:

1. ALL NEW WINDOWS ARE MILGARD STANDARD ALUMINUM.
2. ALL UNITS VIEWED FROM EXTERIOR.
3. DIMENSIONS ARE WINDOW FRAME/DOOR SIZES. CONTRACTOR TO VIF & ALLOW FOR FRAME & SHIM SPACE AS REQ. NOTIFY THE ARCHITECT IF SPECIFIED WINDOW FRAME SIZE DOES NOT FIT AS SCHEDULED.
4. ALL EXTERIOR GLAZING TO BE NFRC APPROVED. DUAL GLAZE LO-E .54 MAX U-FACTOR.
5. ALL GLAZING IN DOORS TO BE TEMPERED UON.
6. ALL DOORS AND WINDOWS HEAD AT 6'-8" EXCEPT NOTED DIFFERENTLY.


REVISIONS	DATE
PERMIT	07.12.19
PERMIT REV.	09.09.19
M. BATH UPDATE	09.16.19
CD SET 25%	09.26.19
CD SET 75%	10.02.19
CD SET 95%	10.04.19
CD SET 100%	10.18.19

SCALE	N-A
SHEET TITLE	

DOOR AND
WINDOW
SCHEDULE

SHEET NUMBER

A7.01

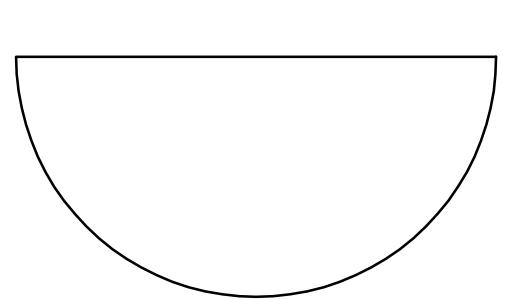

1045 17TH STREET
SUITE 202
SAN FRANCISCO, CA 94107
415.515.0614
REDDOTSTUDIO.COM

red dot studio

ARCHITECTURE AND DESIGN

Project: 620 WALLER STREET DB WINDOWS AND SKYLIGHTS

CODE	LEVEL	RM#	ROOM NAME	OPERATION	SIZE WxH	DESCRIPTION	MODEL	FINISH		VENDOR	HARDWARE				NOTES	
								INTERIOR	EXTERIOR		HARDWARE	HINGE	FINISH	HANDLE		
A1	2	201	KITCHEN	DOUBLE HUNG	2'-10" x 6'-4"	WOOD CLAD WINDOW	ULTIMATE	PT-1	CLAD COLOR TBD	MARVIN WINDOW, INC	TBD	N/A	TBD	TBD	SCREEN	REPLACE IN (E) OPENING Ogee STICKING
A2	2	201	KITCHEN	DOUBLE HUNG	3'-0" x 6'-4"	WOOD CLAD WINDOW	ULTIMATE	PT-1	CLAD COLOR TBD	MARVIN WINDOW, INC	TBD	N/A	TBD	TBD	SCREEN	REPLACE IN (E) OPENING Ogee STICKING
A3	2	201	KITCHEN	DOUBLE HUNG	2'-10" x 6'-4"	WOOD CLAD WINDOW	ULTIMATE	PT-1	CLAD COLOR TBD	MARVIN WINDOW, INC	TBD	N/A	TBD	TBD	SCREEN	REPLACE IN (E) OPENING Ogee STICKING
A4	2	201	KITCHEN	DOUBLE HUNG	3'-6" x 6'-4"	WOOD CLAD WINDOW	ULTIMATE	PT-1	CLAD COLOR TBD	MARVIN WINDOW, INC	TBD	N/A	TBD	TBD	SCREEN	REPLACE IN (E) OPENING Ogee STICKING
A5	2	203	BEDROOM2	DOUBLE HUNG	2'-10" x 6'-4"	WOOD CLAD WINDOW	ULTIMATE	PT-1	CLAD COLOR TBD	MARVIN WINDOW, INC	TBD	N/A	TBD	TBD	SCREEN	REPLACE IN (E) OPENING Ogee STICKING
A6	2	203	BEDROOM2	DOUBLE HUNG	3'-0" x 6'-4"	WOOD CLAD WINDOW	ULTIMATE	PT-1	CLAD COLOR TBD	MARVIN WINDOW, INC	TBD	N/A	TBD	TBD	SCREEN	REPLACE IN (E) OPENING Ogee STICKING
A7	2	203	BEDROOM2	DOUBLE HUNG	2'-10" x 6'-4"	WOOD CLAD WINDOW	ULTIMATE	PT-1	CLAD COLOR TBD	MARVIN WINDOW, INC	TBD	N/A	TBD	TBD	SCREEN	REPLACE IN (E) OPENING Ogee STICKING
A8	2	204	BEDROOM1	DOUBLE HUNG	1'-10" x 6'-4"	WOOD CLAD WINDOW	INTEGRITY	PT-1	CLAD COLOR TBD	MARVIN WINDOW, INC	TBD	N/A	TBD	TBD	SCREEN	REPLACE IN (E) OPENING Ogee STICKING
A9	2	204	BEDROOM1	DOUBLE HUNG	3'-6" x 6'-4"	WOOD CLAD WINDOW	INTEGRITY	PT-1	CLAD COLOR TBD	MARVIN WINDOW, INC	TBD	N/A	TBD	TBD	SCREEN	REPLACE IN (E) OPENING Ogee STICKING
A10	2	204	BEDROOM1	DOUBLE HUNG	1'-10" x 6'-4"	WOOD CLAD WINDOW	INTEGRITY	PT-1	CLAD COLOR TBD	MARVIN WINDOW, INC	TBD	N/A	TBD	TBD	SCREEN	REPLACE IN (E) OPENING Ogee STICKING
A11	2	205	BATH	DOUBLE HUNG	2'-0" x 3'-9"	WOOD CLAD WINDOW	INTEGRITY	PT-1	CLAD COLOR TBD	MARVIN WINDOW, INC	TBD	N/A	TBD	TBD	SCREEN	REPLACE IN (E) OPENING Ogee STICKING
A12	3	207	MECH	FRENCH CASEMENT	3'-6" x 5'-1"	WOOD CLAD WINDOW	INTEGRITY	PT-1	CLAD COLOR TBD	MARVIN WINDOW, INC	TBD	N/A	TBD	TBD	SCREEN	V.I.F IF MARVIN CAN BE INSTALLED
E1	ROOF		ATTIC	ELECTRIC OPERATION	2'-6" x 3'-10"	DECK MOUNTED, SUN CONTROL FILM, NEAT® GLASS		PRE-FINISH WHITE			VELUX	TBD	N/A	TBD	TBD	
E2	ROOF		ATTIC	FIXED	2'-6" x 3'-10"	DECK MOUNTED, SUN CONTROL FILM, NEAT® GLASS		PRE-FINISH WHITE			VELUX	TBD	N/A	TBD	TBD	

D8 DOORS

CODE	LEVEL	RM#	ROOM NAME	OPERATION	SIZE WxH	DESCRIPTION		FINISH		VENDOR	HARDWARE				NOTES	
								INTERIOR	EXTERIOR		HARDWARE	HINGE	FINISH	HANDLE	HANDLE ACCESSORY	
201	2	207	MECH	EXTERIOR - INSWING	2'-6" X 6'-8"	SOLID CORE		PT-1	PT-1	SF WNDOW & DOOR CO	LOCKING	BLACK	BLACK	BLACK		MATCH (E) DOORS
202	2	207	MECH	INTERIOR - OUTSWING	2'-8" X 6'-8"	SOLID CORE		PT-1	PT-1	SF WNDOW & DOOR CO	PASSAGE	BLACK	BLACK	BLACK		MATCH (E) DOORS
203	2	206	KITCHEN	INTERIOR - INSWING	2'-0" X 6'-8"	SOLID CORE		PT-1	PT-1	SF WNDOW & DOOR CO	PASSAGE	BLACK	BLACK	BLACK		MATCH (E) DOORS
204	2	205	KITCHEN	INTERIOR - OUTSWING	2'-6" X 6'-8"	SOLID CORE		PT-1	PT-1	SF WNDOW & DOOR CO	PRIVACY	BLACK	BLACK	BLACK		MATCH (E) DOORS
205	2	204	BEDROOM 1	INTERIOR - INSWING	2'-6" X 6'-8"	SOLID CORE		PT-1	PT-1	SF WNDOW & DOOR CO	PRIVACY	BLACK	BLACK	BLACK		MATCH (E) DOORS
206	2	204	BEDROOM 2	SLIDING PAIR	(2) 3'-0" X 6'-8"	SOLID CORE		PT-1	PT-1	SF WNDOW & DOOR CO	HAEEFELE HAWA	BLACK	BLACK	BLACK		MATCH (E) DOORS
207	2	203	BEDROOM 2	INTERIOR - INSWING	2'-6" X 6'-8"	SOLID CORE		PT-1	PT-1	SF WNDOW & DOOR CO	PRIVACY	BLACK	BLACK	BLACK		MATCH (E) DOORS
208	2	203	BEDROOM 2	INTERIOR - OUTSWING	2'-6" X 6'-8"	SOLID CORE		PT-1	PT-1	SF WNDOW & DOOR CO	PASSAGE	BLACK	BLACK	BLACK		MATCH (E) DOORS
209	2	203	BEDROOM 1	SLIDING PAIR	(2) 3'-0" X 6'-8"	SOLID CORE		PT-1	PT-1	SF WNDOW & DOOR CO	HAEEFELE HAWA	BLACK	BLACK	BLACK		MATCH (E) DOORS

red dot studio
ARCHITECTURE AND DESIGN

1045 17TH STREET
SUITE 202
SAN FRANCISCO, CA 94107
415.515.0614
REDDOTSTUDIO.COM

REVISIONS DATE
PERMIT 01.28.19

SCALE
1/4" = 1'-0"
SHEET TITLE

DOOR AND
WINDOW
SCHEDULE

SHEET NUMBER

A7.01

red dot studio

ARCHITECTURE AND DESIGN

Project: Jensen 2 18th Ave

DB WINDOWS AND SKYLIGHTS

CODE	LEVEL	RMF	ROOM NAME	OPERATION	SIZE WxH	DESCRIPTION	FINISH		VENDOR	HARDWARE	HINGE	FINISH	HANDLE	ACCESSORY	NOTES
							INTERIOR	EXTERIOR							
1-A1	1	101	SPEAKEASY	AWNING	3'-3 1/8" X 2'-0"	WOOD WINDOW	PT-1	PTD - TBD	WOODEN WINDOW, INC.	LEVER AND LOCK	PROVIDED BY MANUFACTURER	BLACK	FORMANI ONE / TBD	FORMANI CASEMENT STAY	MATCH EXISTING MULLION SIZE AND DETAIL
1-A3	1	101	SPEAKEASY	FIXED	3'-3 1/8" X 2'-3 1/2"	WOOD WINDOW	PT-1	PTD - TBD	WOODEN WINDOW, INC.	N/A	N/A	N/A	N/A	N/A	MATCH EXISTING MULLION SIZE AND DETAIL
1-B1	1	101	SPEAKEASY	FIXED	3'-0 5/8" X 2'-0"	WOOD WINDOW	PT-1	PTD - TBD	WOODEN WINDOW, INC.	N/A	N/A	N/A	N/A	N/A	MATCH EXISTING MULLION SIZE AND DETAIL
1-B2	1	101	SPEAKEASY	FIXED	3'-0 5/8" X 7'-3 1/2"	WOOD WINDOW	PT-1	PTD - TBD	WOODEN WINDOW, INC.	N/A	N/A	N/A	N/A	N/A	MATCH EXISTING MULLION SIZE AND DETAIL
1-A2	1	101	SPEAKEASY	AWNING	3'-3 1/8" X 2'-0"	WOOD WINDOW	PT-1	PTD - TBD	WOODEN WINDOW, INC.	LEVER AND LOCK	PROVIDED BY MANUFACTURER	BLACK	FORMANI ONE / TBD	FORMANI CASEMENT STAY	MATCH EXISTING MULLION SIZE AND DETAIL
1-A4	1	101	SPEAKEASY	FIXED	3'-3 1/8" X 2'-3 1/2"	WOOD WINDOW	PT-1	PTD - TBD	WOODEN WINDOW, INC.	N/A	N/A	N/A	N/A	N/A	MATCH EXISTING MULLION SIZE AND DETAIL
1-C1	1	102	OFFICE/GUEST ROOM	CASEMENT	3'-6 3/8" X 5'-0"	WOOD WINDOW	PT-1	PTD - TBD	MARVIN ULTIMATE	LEVER AND LOCK	PROVIDED BY MANUFACTURER	BLACK	FORMANI ONE / TBD	PER MANUFACTURER	CONFIRM W/ WINDOW MNTR SPECIFIED WINDOW HARDWARE WORKS
1-C2	1	102	OFFICE/GUEST ROOM	CASEMENT	3'-6 3/8" X 5'-0"	WOOD WINDOW	PT-1	PTD - TBD	MARVIN ULTIMATE	LEVER AND LOCK	PROVIDED BY MANUFACTURER	BLACK	FORMANI ONE / TBD	PER MANUFACTURER	CONFIRM W/ WINDOW MNTR SPECIFIED WINDOW HARDWARE WORKS
1-C3	1	102	OFFICE/GUEST ROOM	CASEMENT	3'-6 3/8" X 5'-0"	WOOD WINDOW	PT-1	PTD - TBD	MARVIN ULTIMATE	LEVER AND LOCK	PROVIDED BY MANUFACTURER	BLACK	FORMANI ONE / TBD	PER MANUFACTURER	CONFIRM W/ WINDOW MNTR SPECIFIED WINDOW HARDWARE WORKS
1-C4	1	102	OFFICE/GUEST ROOM	CASEMENT	3'-6 3/8" X 5'-0"	WOOD WINDOW	PT-1	PTD - TBD	MARVIN ULTIMATE	LEVER AND LOCK	PROVIDED BY MANUFACTURER	BLACK	FORMANI ONE / TBD	PER MANUFACTURER	CONFIRM W/ WINDOW MNTR SPECIFIED WINDOW HARDWARE WORKS
2-C2	2	201	ENTRY COVE	EXISTING TO REMAIN	2'-11 1/16" X 4'-9 3/4"	WOOD WINDOW (STAINED GLASS)	F-3	PTD - TBD	EXISTING TO REMAIN	EXISTING	EXISTING	EXISTING	EXISTING	EXISTING	
2-C1	2	201	ENTRY COVE	EXISTING TO REMAIN	2'-11 1/16" X 4'-9 3/4"	WOOD WINDOW (STAINED GLASS)	F-3	PTD - TBD	EXISTING TO REMAIN	EXISTING	EXISTING	EXISTING	EXISTING	EXISTING	
2-B1	2	201	ENTRY COVE	DOUBLE HUNG	2'-11 1/16" X 7'-10"	WOOD WINDOW	PT-1	PTD - TBD	MARVIN ULTIMATE	LEVER AND LOCK	PROVIDED BY MANUFACTURER	BLACK	PER MANUFACTURER	N/A	CONFIRM W/ WINDOW MNTR SPECIFIED WINDOW HARDWARE WORKS
2-L4	F	208	KITCHEN	CASEMENT	2'-10 11/16" X 6'-0"	WOOD WINDOW	PT-1	PTD - TBD	MARVIN ULTIMATE	LEVER AND LOCK	PROVIDED BY MANUFACTURER	BLACK	FORMANI ONE / TBD	CONFIRM W/ WINDOW MNTR SPECIFIED WINDOW HARDWARE WORKS	
2-L3	2	208	KITCHEN	CASEMENT	2'-10 11/16" X 6'-0"	WOOD WINDOW	PT-1	PTD - TBD	MARVIN ULTIMATE	LEVER AND LOCK	PROVIDED BY MANUFACTURER	BLACK	FORMANI ONE / TBD	CONFIRM W/ WINDOW MNTR SPECIFIED WINDOW HARDWARE WORKS	
2-L2	2	208	KITCHEN	CASEMENT	2'-10 11/16" X 6'-0"	WOOD WINDOW	PT-1	PTD - TBD	MARVIN ULTIMATE	LEVER AND LOCK	PROVIDED BY MANUFACTURER	BLACK	FORMANI CASEMENT STAY	CONFIRM W/ WINDOW MNTR SPECIFIED WINDOW HARDWARE WORKS	
2-L1	2	208	KITCHEN	CASEMENT	2'-10 11/16" X 6'-0"	WOOD WINDOW	PT-1	PTD - TBD	MARVIN ULTIMATE	LEVER AND LOCK	PROVIDED BY MANUFACTURER	BLACK	FORMANI CASEMENT STAY	CONFIRM W/ WINDOW MNTR SPECIFIED WINDOW HARDWARE WORKS	
2-N1	2	211	EXERCISE ROOM	CASEMENT	3'-8" X 5'-2"	WOOD WINDOW	PT-1	PTD - TBD	MARVIN ULTIMATE	LEVER AND LOCK	PROVIDED BY MANUFACTURER	BLACK	PER MANUFACTURER		
2-N2	2	211	EXERCISE ROOM	FIXED	3'-8" X 5'-2"	WOOD WINDOW	PT-1	PTD - TBD	MARVIN ULTIMATE	N/A	N/A	N/A	N/A	N/A	
2-N3	2	211	EXERCISE ROOM	CASEMENT	3'-8" X 5'-2"	WOOD WINDOW	PT-1	PTD - TBD	MARVIN ULTIMATE	LEVER AND LOCK	PROVIDED BY MANUFACTURER	BLACK	PER MANUFACTURER	PER MANUFACTURER	
2-K1	2	209	SITTING AREA	EXISTING TO REMAIN	7'-5 1/8" X 5'-0"	WOOD WINDOW	PT-1	PTD - TBD	EXISTING TO REMAIN	EXISTING	N/A	N/A	N/A	N/A	MAY REQUIRE REPAIR
2-J1	2	204	DINING ROOM	EXISTING TO REMAIN	7'-10 7/16" X 5'-0"	WOOD WINDOW	F-3	PTD - TBD	EXISTING TO REMAIN	EXISTING	N/A	N/A	N/A	N/A	MAY REQUIRE REPAIR
2-H1	2	202	FOYER	EXISTING TO REMAIN	8'-11 3/16" X 5'-0"	WOOD WINDOW	F-3	PTD - TBD	EXISTING TO REMAIN	EXISTING	N/A	N/A	N/A	N/A	MAY REQUIRE REPAIR
2-F2	2	203	LIVING ROOM	CASEMENT	4'-0" X 5'-0"	WOOD WINDOW	F-3	PTD - TBD	WOODEN WINDOW, INC.	LEVER AND LOCK	PROVIDED BY MANUFACTURER	BLACK	FORMANI ONE / TBD	CONFIRM W/ WINDOW MNTR SPECIFIED WINDOW HARDWARE WORKS	
2-G1	2	203	LIVING ROOM	FIXED	8'-11 3/16" X 5'-0"	WOOD WINDOW	F-3	PTD - TBD	WOODEN WINDOW, INC.	N/A	N/A	N/A	N/A	N/A	
2-F1	2	203	LIVING ROOM	CASEMENT	4'-0" X 5'-0"	WOOD WINDOW	F-3	PTD - TBD	WOODEN WINDOW, INC.	LEVER AND LOCK	PROVIDED BY MANUFACTURER	BLACK	FORMANI ONE / TBD	CONFIRM W/ WINDOW MNTR SPECIFIED WINDOW HARDWARE WORKS	
2-E1	2	203	LIVING ROOM	FIXED	10'-0 1/4" X 6'-0 3/4"	WOOD WINDOW	F-3	PTD - TBD	EXISTING TO REMAIN	EXISTING	N/A	N/A	N/A	N/A	
2-D2	2	203	LIVING ROOM	FIXED	2'-11 1/16" X 2'-0"	WOOD WINDOW	F-3	PTD - TBD	EXISTING TO REMAIN	EXISTING	N/A	N/A	N/A	N/A	
2-D1	2	203	LIVING ROOM	FIXED	2'-11 1/16" X 2'-0"	WOOD WINDOW	F-3	PTD - TBD	EXISTING TO REMAIN	EXISTING	N/A	N/A	N/A	N/A	
3-M1	3	301	UPPER HALL	FIXED	1'-5 1/16" X 3'-10 15/16"	WOOD WINDOW	PT-1	PTD - TBD	EXISTING TO REMAIN	EXISTING	N/A	N/A	N/A	N/A	
3-L1	3	301	UPPER HALL	DOUBLE HUNG	3'-5 3/16" X 5'-0"	WOOD WINDOW	PT-1	PTD - TBD	MARVIN ULTIMATE	PULLS AND LOCK	PROVIDED BY MANUFACTURER	BLACK	PER MANUFACTURER	PER MANUFACTURER	
3-K2	3	305	LAUNDRY	DOUBLE HUNG	2'-4" X 5'-0"	WOOD WINDOW	PT-1	PTD - TBD	MARVIN ULTIMATE	PULLS AND LOCK	PROVIDED BY MANUFACTURER	BLACK	PER MANUFACTURER	PER MANUFACTURER	
3-K1	3	305	LAUNDRY	DOUBLE HUNG	2'-4" X 5'-0"	WOOD WINDOW	PT-1	PTD - TBD	MARVIN ULTIMATE	PULLS AND LOCK	PROVIDED BY MANUFACTURER	BLACK	PER MANUFACTURER	PER MANUFACTURER	
3-J2	3	307	BEDROOM 1	CASEMENT	5'-5 3/16" X 5'-0"	WOOD WINDOW	PT-1	PTD - TBD	MARVIN ULTIMATE	LEVER AND LOCK	PROVIDED BY MANUFACTURER	BLACK	PER MANUFACTURER	PER MANUFACTURER	
3-J1	3	307	BEDROOM 1	CASEMENT	5'-5 3/16" X 5'-0"	WOOD WINDOW	PT-1	PTD - TBD	MARVIN ULTIMATE	LEVER AND LOCK	PROVIDED BY MANUFACTURER	BLACK	PER MANUFACTURER	PER MANUFACTURER	
3-H2	3	307	BEDROOM 1	CASEMENT	3'-10 3/16" X 5'-0"	WOOD WINDOW	PT-1	PTD - TBD	MARVIN ULTIMATE	LEVER AND LOCK	PROVIDED BY MANUFACTURER	BLACK	PER MANUFACTURER	PER MANUFACTURER	EGRESS
3-H1	3	307	BEDROOM 1	CASEMENT	3'-10 3/16" X 5'-0"	WOOD WINDOW	PT-1	PTD - TBD	MARVIN ULTIMATE	LEVER AND LOCK	PROVIDED BY MANUFACTURER	BLACK	PER MANUFACTURER	PER MANUFACTURER	
3-G2	3	308	BEDROOM 2	CASEMENT	3'-5 1/4" X 5'-0"	WOOD WINDOW	PT-1	PTD - TBD	MARVIN ULTIMATE	LEVER AND LOCK	PROVIDED BY MANUFACTURER	BLACK	PER MANUFACTURER	PER MANUFACTURER	
3-G1	3	308	BEDROOM 2	CASEMENT	3'-5 1/4" X 5'-0"	WOOD WINDOW	PT-1	PTD - TBD	MARVIN ULTIMATE	LEVER AND LOCK	PROVIDED BY MANUFACTURER	BLACK	PER MANUFACTURER	PER MANUFACTURER	
3-F2	3	308	BEDROOM 2	CASEMENT	3'-5 1/4" X 5'-0"	WOOD WINDOW	PT-1	PTD - TBD	MARVIN ULTIMATE	LEVER AND LOCK	PROVIDED BY MANUFACTURER	BLACK	PER MANUFACTURER	PER MANUFACTURER	
3-F1	3	308	BEDROOM 2	CASEMENT	3'-5 1/4" X 5'-0"	WOOD WINDOW	PT-1	PTD - TBD	MARVIN ULTIMATE	LEVER AND LOCK	PROVIDED BY MANUFACTURER	BLACK	PER MANUFACTURER	PER MANUFACTURER	EGRESS
3-E2	3	308	MASTER BATHROOM	CASEMENT	3'-4 15/16" X 5'-0"	WOOD WINDOW	PT-1	PTD - TBD	MARVIN ULTIMATE	LEVER AND LOCK	PROVIDED BY MANUFACTURER	BLACK	FORMANI ONE / TBD	CONFIRM W/ WINDOW MNTR SPECIFIED WINDOW HARDWARE WORKS	
3-E1	3	308	MASTER BATHROOM	CASEMENT	3'-4 15/16" X 5'-0"	WOOD WINDOW	PT-1	PTD - TBD	MARVIN ULTIMATE	LEVER AND LOCK	PROVIDED BY MANUFACTURER	BLACK	FORMANI ONE / TBD	CONFIRM W/ WINDOW MNTR SPECIFIED WINDOW HARDWARE WORKS	
3-D1	3	307	MASTER BEDROOM	CASEMENT	4'-0" X 4'-0"	WOOD WINDOW	PT-1	PTD - TBD	MARVIN ULTIMATE	LEVER AND LOCK	PROVIDED BY MANUFACTURER	BLACK	FORMANI ONE / TBD	CONFIRM W/ WINDOW MNTR SPECIFIED WINDOW HARDWARE WORKS	
3-B2	3	302	MASTER BEDROOM	CASEMENT	3'-10 1/8" X 5'-0"	WOOD WINDOW	PT-1	PTD - TBD	WOODEN WINDOW, INC.	LEVER AND LOCK	PROVIDED BY MANUFACTURER	BLACK	FORMANI ONE / TBD	CONFIRM W/ WINDOW MNTR SPECIFIED WINDOW HARDWARE WORKS	
3-C1	3	302	MASTER BEDROOM	FIXED	8'-11 3/16" X 5'-0"	WOOD WINDOW	PT-1	PTD - TBD	WOODEN WINDOW, INC.	N/A	N/A	N/A	N/A	N/A	
3-B1	3	302	MASTER BEDROOM	CASEMENT	4'-0" X 5'-0"	WOOD WINDOW	PT-1	PTD - TBD	WOODEN WINDOW, INC.	LEVER AND LOCK	PROVIDED BY MANUFACTURER</				


CODE	LEVEL	RM#	ROOM NAME	OPERATION	SIZE WxH	DESCRIPTION	FINISH INTERIOR	EXTERIOR	VENDOR	HARDWARE	HINGE	FINISH	HANDLE	ACCESSORY	NOTES
1-A	1	102	MASTER BEDROOM	CASEMENT / FIXED	3'-6" x 7'-6"	WOOD WINDOW	PTD - TBD	PTD - TBD	MARVIN WINDOW, INC	TBD	N/A	TBD	TBD		EGRESS WINDOW
2-B	2	207	BREAKFAST NOOK	CASEMENT / FIXED	3'-6" x 7'-6"	WOOD WINDOW	PTD - TBD	PTD - TBD	MARVIN WINDOW, INC	TBD	N/A	TBD	TBD		
2-C	2	207	BREAKFAST NOOK	CASEMENT / FIXED	3'-6" x 7'-6"	WOOD WINDOW	PTD - TBD	PTD - TBD	MARVIN WINDOW, INC	TBD	N/A	TBD	TBD		
S-1	2	205	SPEAKEASY	ELECTRIC OPERATOR	VCE 3046	WOOD WINDOW	PTD - TBD	PTD - TBD	VELUX	TBD	N/A	TBD	TBD		
S-2	2	205	SPEAKEASY	ELECTRIC OPERATOR	VCE 3046	WOOD WINDOW	PTD - TBD	PTD - TBD	VELUX	TBD	N/A	TBD	TBD		
S-3	2	206	SPEAKEASY	ELECTRIC OPERATOR	VCE 3046	WOOD WINDOW	PTD - TBD	PTD - TBD	VELUX	TBD	N/A	TBD	TBD		
S-4	2	206	SPEAKEASY	ELECTRIC OPERATOR	VCE 3046	WOOD WINDOW	PTD - TBD	PTD - TBD	VELUX	TBD	N/A	TBD	TBD		

DB DOORS


CODE	LEVEL	RM#	ROOM NAME	OPERATION	SIZE WxH	DESCRIPTION	FINISH INTERIOR	EXTERIOR	VENDOR	HARDWARE	HINGE	FINISH	HANDLE	HANDLE ACCESSORY	NOTES
101	1	101	READING NOOK	EXTERIOR - INSWING	3'-0" X 6'-8"	WOOD AND GLASS	PTD - TBD	PTD - TBD	SF WNDOW & DOOR CO	LOCKING	ALL BRASS SQ 4X4 BUTT HINGE	TBD	TBD		
102	1	105	GARAGE	INTERIOR - INSWING	2'-8" X 6'-8"	20 MINUTE FIRE RATED	PTD - TBD	PTD - TBD	SF WNDOW & DOOR CO	LOCKING	ALL BRASS SQ 4X4 BUTT HINGE	TBD	TBD		20 MINUTE FIRE RATED
103	1	102	MASTER BEDROOM	INTRIOR BARN DOOR	2'-8" X 6'-8"	TOP HUNG BARN DOOR	PTD - TBD	PTD - TBD	REAL SLIDING HARDWARE	PRIVACY	AERO FLAT TRACK KIT	TBD	TBD		HORIZONTAL DOUGLASS FIR WITH AERO FLAT TRACK HARDWARE KIT
104	1	103	MASTER CLOSET	SLIDING POCKET	2'-8" X 6'-8"	POCKET DOOR	PTD - TBD	PTD - TBD	SF WNDOW & DOOR CO	PASSAGE	TOP HUNG SLIDING	TBD	TBD		
105	1	104	MASTER BATH	SLIDING POCKET	2'-8" X 6'-8"	POCKET DOOR	PTD - TBD	PTD - TBD	SF WNDOW & DOOR CO	PRIVACY	TOP HUNG SLIDING	TBD	TBD		
201	2	204	BATH 1	INTERIOR - INSWING	2'-6" X 6'-8"	SOLID CORE	PTD - TBD	PTD - TBD	SF WNDOW & DOOR CO	PRIVACY	ALL BRASS SQ 4X4 BUTT HINGE	TBD	TBD		
202	2	203	GUEST CLOSET	INTERIOR - OUTSWING	2'-6" X 6'-8"	SOLID CORE	PTD - TBD	PTD - TBD	SF WNDOW & DOOR CO	PASSAGE	ALL BRASS SQ 4X4 BUTT HINGE	TBD	TBD		

red dot studio
ARCHITECTURE AND DESIGN1045 17TH STREET
SUITE 202
SAN FRANCISCO, CA 94107
415.515.0614


REDDOTSTUDIO.COM

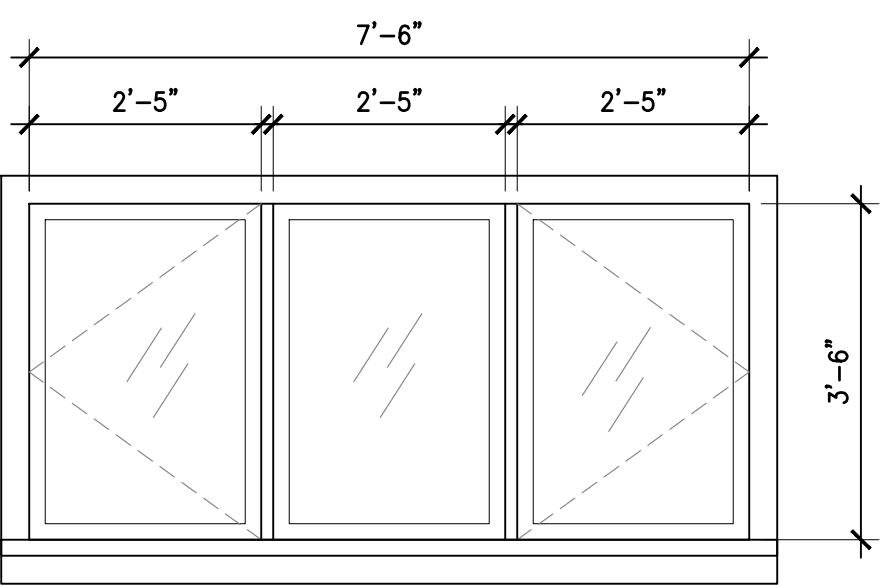


WINDOW TYPES 1/2" SCALE

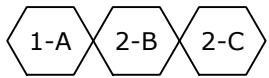

TYPE: NEW WINDOWS
OPERATION: CASEMENT/FIXED
MATERIAL: WOOD & GLASS
FINISH: PAINTED
GLAZING: LOW-E, DUAL PANE
MANUFACTURER: MARVIN WINDOWS
MODEL: ULTIMATE CLAD
NOTES: EGRESS PER PLAN

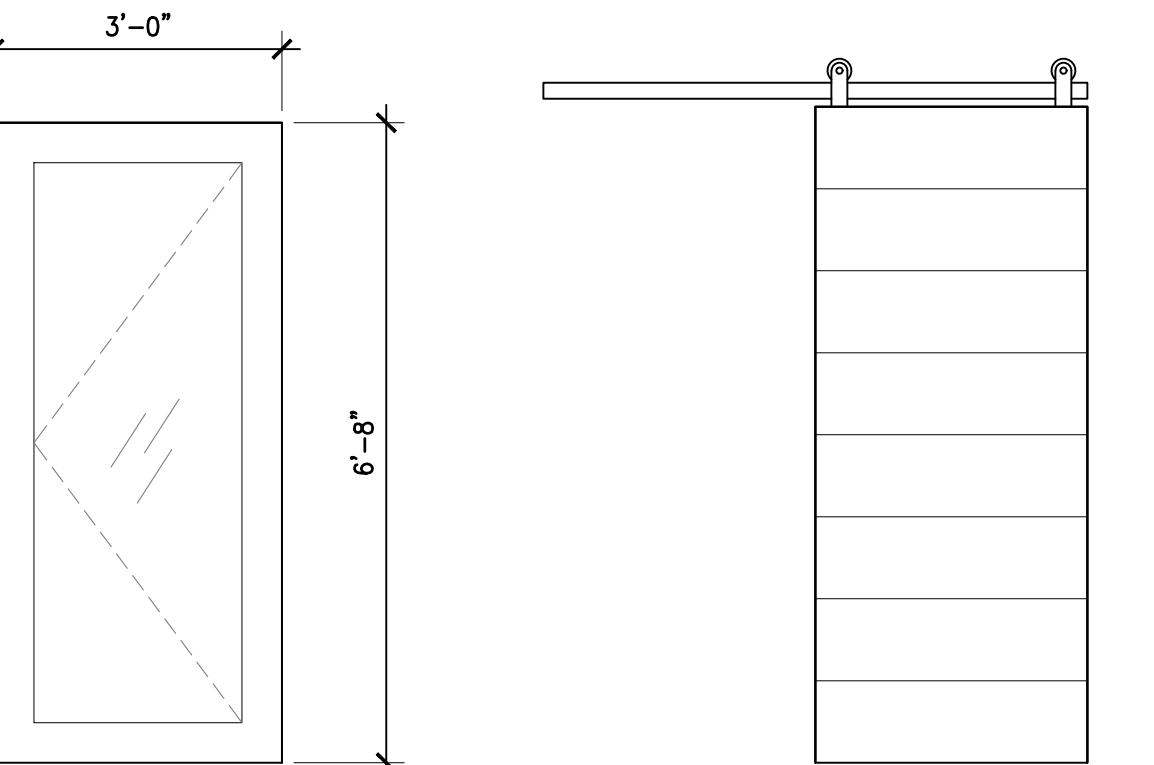

DOOR TYPES 1/2" SCALE

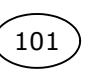

TYPE: EXTERIOR DOOR
OPERATION: INSWING
MATERIAL: WOOD & GLASS
FINISH: PAINTED
GLAZING: LOW-E, DUAL PANE
MANUFACTURER: SF WINDOW & DOOR CO
MODEL: GLAZED DOOR
NOTES:



TYPE: BARN DOOR
OPERATION: TOP HUNG
MATERIAL: WOOD
FINISH: STAINED WOOD
GLAZING: NA
MANUFACTURER: REAL SLIDING HARDWARE
MODEL: HORIZONTAL PLANK
NOTES: SEE DOOR SCHEDULE

REVISIONS DATE
DD BID SET 04.09.18SCALE
AS NOTED

SHEET TITLE

DOOR
WINDOW &
SKYLIGHT
SCHEDULE

SHEET NUMBER

A7.01

CODE	LEVEL	RM#	ROOM NAME	OPERATION	SIZE WxH	DESCRIPTION	MODEL	FINISH		VENDOR	HARDWARE				NOTES
								INTERIOR	EXTERIOR		HARDWARE	HINGE	FINISH	HANDLE	ACCESSORY
A4	2	201	ENTRY	FIXED	1'-11" X 2'-11"	WOOD CLAD	PT	BLK	BLK	MARVIN ULTIMATE	N/A	BLK	BLK	N/A	(N) WINDOW TO REPLACE IN KIND, HANG ORIGINAL STAIN GLASS BEHIND WINDOW
					2'-6 1/2" X 6'-4"										
A5	2	202	DINING ROOM	DOUBLE HUNG	1/4"	WOOD CLAD	PT	BLK	BLK	MARVIN ULTIMATE	LOCKING	BLK	BLK	STANDARD	(N) WINDOW TO REPLACE IN KIND
A6	2	202	DINING ROOM	DOUBLE HUNG	4'-2" X 6'-4"	WOOD CLAD	PT	BLK	BLK	MARVIN ULTIMATE	LOCKING	BLK	BLK	STANDARD	(N) WINDOW TO REPLACE IN KIND
A7	2	202	DINING ROOM	DOUBLE HUNG	2'-6 1/2" X 6'-4"										
					1/4"	WOOD CLAD	PT	BLK	BLK	MARVIN ULTIMATE	LOCKING	BLK	BLK	STANDARD	(N) WINDOW TO REPLACE IN KIND
A8	3	302	MASTER BEDROOM	DOUBLE HUNG	1/2"	WOOD CLAD	PT	BLK	BLK	MARVIN ULTIMATE	LOCKING	BLK	BLK	STANDARD	(N) WINDOW TO REPLACE IN KIND
A9	3	302	MASTER BEDROOM	DOUBLE HUNG	2'-5" X 5'-8 1/2"	WOOD CLAD	PT	BLK	BLK	MARVIN ULTIMATE	LOCKING	BLK	BLK	STANDARD	(N) WINDOW TO REPLACE IN KIND
A10	3	302	MASTER BEDROOM	DOUBLE HUNG	1/2"	WOOD CLAD	PT	BLK	BLK	MARVIN ULTIMATE	LOCKING	BLK	BLK	STANDARD	(N) WINDOW TO REPLACE IN KIND
A11	3	302	MASTER BEDROOM	DOUBLE HUNG	2'-0" X 3'-4 3/4"	WOOD CLAD	PT	BLK	BLK	MARVIN ULTIMATE	LOCKING	BLK	BLK	STANDARD	(N) WINDOW TO REPLACE IN KIND
E2	ROOF	N/A	N/A	FIXED	30 1/2" X 46 1/2"	CURB MOUNTED, SUN CONTROL FILM, NEAT® GLASS	PRE-FINISH WHITE	VELUX	N/A	VELUX	N/A	BLK	BLK	N/A	(N) SKYLIGHT
E3	ROOF	N/A	N/A	OPERABLE	30 1/2" X 46 1/2"	CURB MOUNTED, SUN CONTROL FILM, NEAT® GLASS	PRE-FINISH WHITE	VELUX	N/A	VELUX	N/A	BLK	BLK	N/A	INSECT SCREEN BLACKOUT BLINDS, INSECT
E4	ROOF	N/A	N/A	OPERABLE	30 1/2" X 46 1/2"	CURB MOUNTED, SUN CONTROL FILM, NEAT® GLASS	PRE-FINISH WHITE	VELUX	N/A	VELUX	N/A	BLK	BLK	N/A	SCREEN (N) SKYLIGHT
E5	ROOF	N/A	N/A	FIXED	30 1/2" X 46 1/2"	CURB MOUNTED, SUN CONTROL FILM, NEAT® GLASS	PRE-FINISH WHITE	VELUX	N/A	VELUX	N/A	BLK	BLK	N/A	BLACKOUT BLINDS (N) SKYLIGHT
E6	ROOF	N/A	N/A	OPERABLE	30"X30"	CURB MOUNTED, SUN CONTROL FILM, NEAT® GLASS	PRE-FINISH WHITE	VELUX	N/A	VELUX	N/A	BLK	BLK	N/A	INSECT SCREEN (N) SKYLIGHT
D8 DOORS															
CODE	LEVEL	RM#	ROOM NAME	OPERATION	SIZE WxH	DESCRIPTION	MODEL	FINISH		VENDOR	HARDWARE				NOTES
								INTERIOR	EXTERIOR		HARDWARE	HINGE	FINISH	HANDLE	
206	2	201	CLOSET	POCKET DOOR	3'-0" X 6'-8"	SOLID CORE PAINTED DOOR	PT	PT	CONTRACTOR CHOICE	PASSAGE	V.I.F				
207	2	205	POWDER RM	OUTSWING - SEE PLAN	2'-0" X 6'-8"	SOLID CORE PAINTED DOOR	PT	PT	CONTRACTOR CHOICE	PRIVACY					
208	2	205	KITCHEN	OUTSWING - SEE PLAN	2'-6" X 6'-8"	SOLID CORE PAINTED DOOR	PT	PT	CONTRACTOR CHOICE	PASSAGE					
301	3	302	MASTER BEDROM	INSWING - SEE PLAN	2'-0" X 6'-8"	SOLID CORE PAINTED DOOR	PT	PT	CONTRACTOR CHOICE	PASSAGE					
302	3	302	MASTER BEDROM	INSWING - SEE PLAN	(2)2'-6" X 6'-8"	SOLID CORE PAINTED DOOR	PT	PT	CONTRACTOR CHOICE	PASSAGE					
303	3	302	MASTER BEDROM	POCKET DOOR	3'-8 3/4" X 6'-8"	SOLID CORE PAINTED DOOR	PT	PT	CONTRACTOR CHOICE	PASSAGE	V.I.F				
304	3	303	STUDY	POCKET DOOR	2'-6" X 6'-8"	SOLID CORE PAINTED DOOR	PT	PT	CONTRACTOR CHOICE	PRIVACY					
305	3	304	BEDROOM 2	INSWING - SEE PLAN	2'-6" X 6'-8"	SOLID CORE PAINTED DOOR	PT	PT	CONTRACTOR CHOICE	PRIVACY					
306	3	304	BEDROOM 2	INSWING - SEE PLAN	2'-6" X 6'-8"	SOLID CORE PAINTED DOOR	PT	PT	CONTRACTOR CHOICE	PASSAGE					
307	3	304	BATH	INSWING - SEE PLAN	2'-6" X 6'-8"	SOLID CORE PAINTED DOOR	PT	PT	CONTRACTOR CHOICE	PRIVACY					
308	3	305	MASTER BATH	INSWING - SEE PLAN	2'-6" X 6'-8"	SOLID CORE PAINTED DOOR	PT	PT	CONTRACTOR CHOICE	PRIVACY					
309	3	305	MASTER BATH	INSWING - SEE PLAN	2'-4" X 6'-8"	SOLID CORE PAINTED DOOR	PT	PT	CONTRACTOR CHOICE	PRIVACY					

red dot studio
ARCHITECTURE AND DESIGN

1045 17TH STREET
SUITE 202
SAN FRANCISCO, CA 94107
415.515.0614

REDDOTSTUDIO.COM

REVISIONS DATE
PERMIT 06.19.18
PHASE 2 BID 09.23.19
CD SET 02.20.20

SCALE
AS NOTED
SHEET TITLE

DOOR &
WINDOW
SCHEDULE

SHEET NUMBER

A7.01

D8 WINDOWS AND SKYLIGHTS

CODE	LEVEL	RM#	ROOM NAME	OPERATION	OPENING SIZE TOTAL	SIZE WXH	DESCRIPTION	MODEL	FINISH		VENDOR	HARDWARE				NOTES	
									INTERIOR	EXTERIOR		HARDWARE	HINGE	FINISH	HANDLE	ACCESSORY	
A1	4	403	LANDING	FIXED		2'-1"- X 3'-4"	PAINTED WOOD WINDOW	ULTIMATE	PRE-PRIMED	BRONZE	MARVIN						SOUTH ELEVATION
A2	4	403	LANDING	FIXED		2'-1"- X 3'-4"	PAINTED WOOD WINDOW	ULTIMATE	PRE-PRIMED	BRONZE	MARVIN						SOUTH ELEVATION
A3	4	403	LANDING	FIXED		2'-1"- X 3'-4"	PAINTED WOOD WINDOW	ULTIMATE	PRE-PRIMED	BRONZE	MARVIN						SOUTH ELEVATION
A4	4	403	LANDING	FIXED		2'-1"- X 3'-4"	PAINTED WOOD WINDOW	ULTIMATE	PRE-PRIMED	BRONZE	MARVIN						SOUTH ELEVATION
A5	4	403	LANDING	FIXED		2'-1"- X 3'-4"	PAINTED WOOD WINDOW	ULTIMATE	PRE-PRIMED	BRONZE	MARVIN						SOUTH ELEVATION
A6	4	403	LANDING	FIXED		2'-1"- X 3'-4"	PAINTED WOOD WINDOW	ULTIMATE	PRE-PRIMED	BRONZE	MARVIN						SOUTH ELEVATION
B1	4	403	LANDING	FIXED		2'-1"- X 1'-7 1/2"	PAINTED WOOD WINDOW	ULTIMATE	PRE-PRIMED	BRONZE	MARVIN						SOUTH ELEVATION
B2	4	403	LANDING	FIXED		2'-1"- X 1'-7 1/2"	PAINTED WOOD WINDOW	ULTIMATE	PRE-PRIMED	BRONZE	MARVIN						SOUTH ELEVATION
B3	4	403	LANDING	FIXED		2'-1"- X 1'-7 1/2"	PAINTED WOOD WINDOW	ULTIMATE	PRE-PRIMED	BRONZE	MARVIN						SOUTH ELEVATION
B4	4	403	LANDING	FIXED		2'-1"- X 1'-7 1/2"	PAINTED WOOD WINDOW	ULTIMATE	PRE-PRIMED	BRONZE	MARVIN						SOUTH ELEVATION
B5	4	403	LANDING	FIXED		2'-1"- X 1'-7 1/2"	PAINTED WOOD WINDOW	ULTIMATE	PRE-PRIMED	BRONZE	MARVIN						SOUTH ELEVATION
B6	4	403	LANDING	FIXED		2'-1"- X 1'-7 1/2"	PAINTED WOOD WINDOW	ULTIMATE	PRE-PRIMED	BRONZE	MARVIN						SOUTH ELEVATION
C1	4	404	BATHROOM	CASEMENT		2'-0"- X 4'-4"	PAINTED WOOD WINDOW	ULTIMATE	PRE-PRIMED	BRONZE	MARVIN			OIL RUBBED BRONZE	FOLGING HANDLE		SOUTH ELEVATION
D1	2	202	FAMILY ROOM	FIXED		2'-11"- X 3'-10"	PAINTED WOOD WINDOW	ULTIMATE	PRE-PRIMED	BRONZE	MARVIN						WEST ELEVATION
D2	2	202	FAMILY ROOM	FIXED		2'-11"- X 3'-10"	PAINTED WOOD WINDOW	ULTIMATE	PRE-PRIMED	BRONZE	MARVIN						WEST ELEVATION
D3	2	202	FAMILY ROOM	FIXED		2'-11"- X 3'-10"	PAINTED WOOD WINDOW	ULTIMATE	PRE-PRIMED	BRONZE	MARVIN						WEST ELEVATION
D4	2	202	FAMILY ROOM	FIXED		2'-11"- X 3'-10"	PAINTED WOOD WINDOW	ULTIMATE	PRE-PRIMED	BRONZE	MARVIN						WEST ELEVATION
E1	2	202	FAMILY ROOM	FIXED	18'-3 5/8" X 8'-8" (6 EQ PANELS)	3'-0 1/4" X 8'-8"	ALUMINUM SLIDING DOOR SYSTEM					BRONZE	FLEETWOOD				NORTH ELEVATION
E2	2	202	FAMILY ROOM	SLIDER	18'-3 5/8" X 8'-8" (6 EQ PANELS)	3'-0 1/4" X 8'-8"	ALUMINUM SLIDING DOOR SYSTEM					BRONZE	FLEETWOOD				NORTH ELEVATION
E3	2	202	FAMILY ROOM	SLIDER	18'-3 5/8" X 8'-8" (6 EQ PANELS)	3'-0 1/4" X 8'-8"	ALUMINUM SLIDING DOOR SYSTEM					BRONZE	FLEETWOOD				NORTH ELEVATION
E4	2	202	FAMILY ROOM	SLIDER	18'-3 5/8" X 8'-8" (6 EQ PANELS)	3'-0 1/4" X 8'-8"	ALUMINUM SLIDING DOOR SYSTEM					BRONZE	FLEETWOOD				NORTH ELEVATION
E5	2	202	FAMILY ROOM	SLIDER	18'-3 5/8" X 8'-8" (6 EQ PANELS)	3'-0 1/4" X 8'-8"	ALUMINUM SLIDING DOOR SYSTEM					BRONZE	FLEETWOOD				NORTH ELEVATION
E6	2	202	FAMILY ROOM	FIXED	18'-3 5/8" X 8'-8" (6 EQ PANELS)	3'-0 1/4" X 8'-8"	ALUMINUM SLIDING DOOR SYSTEM					BRONZE	FLEETWOOD				NORTH ELEVATION
E7	3	301	BEDROOM 1	FIXED	18'-3 5/8" X 8'-0" (6 EQ PANELS)	3'-0 1/4" X 8'-0"	ALUMINUM SLIDING DOOR SYSTEM					BRONZE	FLEETWOOD				NORTH ELEVATION
E8	3	301	BEDROOM 1	SLIDER	18'-3 5/8" X 8'-0" (6 EQ PANELS)	3'-0 1/4" X 8'-0"	ALUMINUM SLIDING DOOR SYSTEM					BRONZE	FLEETWOOD				NORTH ELEVATION
E9	3	301	BEDROOM 1	SLIDER	18'-3 5/8" X 8'-0" (6 EQ PANELS)	3'-0 1/4" X 8'-0"	ALUMINUM SLIDING DOOR SYSTEM					BRONZE	FLEETWOOD				NORTH ELEVATION
E10	3	301	BEDROOM 1	SLIDER	18'-3 5/8" X 8'-0" (6 EQ PANELS)	3'-0 1/4" X 8'-0"	ALUMINUM SLIDING DOOR SYSTEM					BRONZE	FLEETWOOD				NORTH ELEVATION
E11	3	301	BEDROOM 1	SLIDER	18'-3 5/8" X 8'-0" (6 EQ PANELS)	3'-0 1/4" X 8'-0"	ALUMINUM SLIDING DOOR SYSTEM					BRONZE	FLEETWOOD				NORTH ELEVATION
E12	3	301	BEDROOM 1	FIXED	18'-3 5/8" X 8'-0" (6 EQ PANELS)	3'-0 1/4" X 8'-0"	ALUMINUM SLIDING DOOR SYSTEM					BRONZE	FLEETWOOD				NORTH ELEVATION
F1	4	401	MASTER BEDROOM	GLASS DOOR	15'-1 1/8" X 8'-1" (5 EQ PANELS)	3'-0 1/4" X 8'-1"	ALUMINUM DOOR SYSTEM					BRONZE	FLEETWOOD				NORTH ELEVATION
F2	4	401	MASTER BEDROOM	GLASS DOOR	15'-1 1/8" X 8'-1" (5 EQ PANELS)	3'-0 1/4" X 8'-1"	ALUMINUM DOOR SYSTEM					BRONZE	FLEETWOOD				NORTH ELEVATION
F3	4	401	MASTER BEDROOM	FIXED	15'-1 1/8" X 8'-1" (5 EQ PANELS)	3'-0 1/4" X 8'-1"	ALUMINUM DOOR SYSTEM					BRONZE	FLEETWOOD				NORTH ELEVATION
F4	4	401	MASTER BEDROOM	GLASS DOOR	15'-1 1/8" X 8'-1" (5 EQ PANELS)	3'-0 1/4" X 8'-1"	ALUMINUM DOOR SYSTEM					BRONZE	FLEETWOOD				NORTH ELEVATION
F5	4	401	MASTER BEDROOM	GLASS DOOR	15'-1 1/8" X 8'-1" (5 EQ PANELS)	3'-0 1/4" X 8'-1"	ALUMINUM DOOR SYSTEM					BRONZE	FLEETWOOD				NORTH ELEVATION
H1	2	201	FAMILY DINING	FIXED		2'-6 5/8" X 6'-10 1/2"	PAINTED WOOD WINDOW	ULTIMATE	PRE-PRIMED	BRONZE	MARVIN						NORTH ELEVATION
H2	3	304	BEDROOM 2	CASEMENT		2'-6 5/8" X 5'-0"	PAINTED WOOD WINDOW	ULTIMATE	PRE-PRIMED	BRONZE	MARVIN			OIL RUBBED BRONZE	FOLGING HANDLE		NORTH ELEVATION
H3	4	401	MASTER BEDROOM	CASEMENT		2'-6 5/8" X 5'-1"	PAINTED WOOD WINDOW	ULTIMATE	PRE-PRIMED	BRONZE	MARVIN			OIL RUBBED BRONZE	FOLGING HANDLE		NORTH ELEVATION
G1	3	301	BEDROOM 1	FIXED	8'-4 7/8" X 5'-1" (3 EQ WINDOWS)	2'-8 1/4" X 5'-1"	PAINTED WOOD WINDOW	ULTIMATE	PRE-PRIMED	BRONZE	MARVIN						EAST ELEVATION
G2	3	301	BEDROOM 1	FIXED	8'-4 7/8" X 5'-1" (3 EQ WINDOWS)	2'-8 1/4" X 5'-1"	PAINTED WOOD WINDOW	ULTIMATE	PRE-PRIMED	BRONZE	MARVIN						EAST ELEVATION
G3	3	301	BEDROOM 1	FIXED	8'-4 7/8" X 5'-1" (3 EQ WINDOWS)	2'-8 1/4" X 5'-1"	PAINTED WOOD WINDOW	ULTIMATE	PRE-PRIMED	BRONZE	MARVIN						EAST ELEVATION
G4	4	401	MASTER BEDROOM	FIXED	4'-7 5/8" X 6'-3 1/2" (2 EQ WINDOWS)	2'-3 7/8" X 6'-3 1/2"	PAINTED WOOD WINDOW	ULTIMATE	PRE-PRIMED	BRONZE	MARVIN						EAST ELEVATION
G5	4	401	MASTER BEDROOM	FIXED	4'-7 5/8" X 6'-3 1/2" (2 EQ WINDOWS)	2'-3 7/8" X 6'-3 1/2"	PAINTED WOOD WINDOW	ULTIMATE	PRE-PRIMED	BRONZE	MARVIN						EAST ELEVATION
D5	3	304	BEDROOM 2	FIXED	4'-7 5/8" X 2'-0" (2 EQ WINDOWS)	2'-3 7/8" X 2'-0"	PAINTED WOOD WINDOW	ULTIMATE	PRE-PRIMED	BRONZE	MARVIN						EAST ELEVATION
D6	3	304	BEDROOM 2	FIXED	4'-7 5/8" X 2'-0" (2 EQ WINDOWS)	2'-3 7/8" X 2'-0"	PAINTED WOOD WINDOW	ULTIMATE	PRE-PRIMED	BRONZE	MARVIN						EAST ELEVATION
D7	3	304	BEDROOM 2	FIXED	4'-7 5/8" X 2'-0" (2 EQ WINDOWS)	2'-3 7/8" X 2'-0"	PAINTED WOOD WINDOW	ULTIMATE	PRE-PRIMED	BRONZE	MARVIN						EAST ELEVATION
D8	3	304	BEDROOM 2	FIXED	4'-7 5/8" X 2'-0" (2 EQ WINDOWS)	2'-3 7/8" X 2'-0"	PAINTED WOOD WINDOW	ULTIMATE	PRE-PRIMED	BRONZE	MARVIN						EAST ELEVATION
SK1	ROOF	NA		FIXED	9'-6 1/4" X 4'-0"		10 ALUMINUM PANELS					BRONZE	CUSTOM				SITE PLAN
SK2	ROOF	NA		FIXED	4'-0" X 10'-3"		10 ALUMINUM PANELS					BRONZE	CUSTOM				SITE PLAN


1045 17TH STREET
SUITE 202
SAN FRANCISCO, CA 94107
415.515.0614

REDDOTSTUDIO.COM


CODE	LEVEL	RM#	ROOM NAME	OPERATION	SIZE WxH	DESCRIPTION	MODEL	FINISH		VENDOR	HARDWARE			NOTES	
								INTERIOR	EXTERIOR		HARDWARE	HINGE	FINISH	HANDLE	
A1	1	104	UNIT 1 BATH	AWNING	3'-0" X 1'-6"	ALUMINUM WINDOWS	450-T	CLEAR ANODIZED	CLEAR ANODIZED	FLEETWOOD	SATIN NICKEL/SILVER				
A2	1	105	UNIT 1 BEDROOM	CASEMENT	2'-6" X 5'-0"	ALUMINUM WINDOWS	450-T	CLEAR ANODIZED	CLEAR ANODIZED	FLEETWOOD	SATIN NICKEL/SILVER	CAM HANDLE			EGRESS WINDOW
A3	1	105	UNIT 1 BEDROOM	FIXED	2'-6" X 5'-0"	ALUMINUM WINDOWS	450-T	CLEAR ANODIZED	CLEAR ANODIZED	FLEETWOOD	SATIN NICKEL/SILVER	CAM HANDLE			
A4	1	103	UNIT 1	CASEMENT	2'-6" X 5'-0"	ALUMINUM WINDOWS	450-T	CLEAR ANODIZED	CLEAR ANODIZED	FLEETWOOD	SATIN NICKEL/SILVER	CAM HANDLE			
B1	2	203	STUDY NOOK	CASEMENT	2'-6" X 5'-0"	WOOD WINDOWS	ACCOYA	WOOD	WOOD	LOEWEN	SATIN NICKEL	CONTEMPORARY			TRANQUILITY GLASS
B2	2	203	STUDY NOOK	FIXED	2'-0" X 6'-6"	WOOD WINDOWS	ACCOYA	WOOD	WOOD	LOEWEN	SATIN NICKEL	CONTEMPORARY			TRANQUILITY GLASS
B3	2	202	LIVING ROOM	OPERABLE TRANSOM	2'-6" X 6'-6"	WOOD WINDOWS	ACCOYA	WOOD	WOOD	LOEWEN	SATIN NICKEL	CONTEMPORARY			TRANQUILITY GLASS
B4	2	202	LIVING ROOM	OPERABLE TRANSOM	2'-6" X 6'-6"	WOOD WINDOWS	ACCOYA	WOOD	WOOD	LOEWEN	SATIN NICKEL	CONTEMPORARY			TRANQUILITY GLASS
B5	2	202	LIVING ROOM	OPERABLE TRANSOM	2'-6" X 6'-6"	WOOD WINDOWS	ACCOYA	WOOD	WOOD	LOEWEN	SATIN NICKEL	CONTEMPORARY			TRANQUILITY GLASS
B6	2	201	STAIR HALL	FIXED FIRE RATED WINDOW	3'-1 3/8" X 8'-7" (X4 PANELS)	1-HR FIRE RATED ALUMINUM WINDOWS	SUPERLITE II XL-60 EXTERIOR	CLEAR ANODIZED	CLEAR ANODIZED	SAFTIFIRST					TRANSLUCENT GLASS 1-HR FIRE RATED. DEDUCT ALTERNATE WIRE GLASS
B7	2	206	DINING ROOM	OPERABLE TRANSOM	2'-6" X 8'-0"	ALUMINUM WINDOWS	450-T	CLEAR ANODIZED	CLEAR ANODIZED	FLEETWOOD	SATIN NICKEL/SILVER	CAM HANDLE			
B8	2	207	KITCHEN	OPERABLE TRANSOM	2'-6" X 8'-0"	ALUMINUM WINDOWS	450-T	CLEAR ANODIZED	CLEAR ANODIZED	FLEETWOOD	SATIN NICKEL/SILVER	CAM HANDLE			
B9	2	207	KITCHEN	OPERABLE TRANSOM	2'-6" X 8'-0"	ALUMINUM WINDOWS	450-T	CLEAR ANODIZED	CLEAR ANODIZED	FLEETWOOD	SATIN NICKEL/SILVER	CAM HANDLE			
B10	2	205	PANTRY	AWNING	2'-0" X 1'-6"	ALUMINUM WINDOWS	450-T	CLEAR ANODIZED	CLEAR ANODIZED	FLEETWOOD	SATIN NICKEL/SILVER	CAM HANDLE			
C1	3	305	BEDROOM 2	CASEMENT	2'-6" X 5'-0"	WOOD WINDOWS	ACCOYA	WOOD	WOOD	LOEWEN	SATIN NICKEL	CONTEMPORARY			EGRESS WINDOW
C2	3	305	BEDROOM 2	FIXED	2'-0" X 5'-0"	WOOD WINDOWS	ACCOYA	WOOD	WOOD	LOEWEN	SATIN NICKEL	CONTEMPORARY			TRANQUILITY GLASS
C3	3	304	BEDROOM 1	CASEMENT	2'-6" X 5'-0"	WOOD WINDOWS	ACCOYA	WOOD	WOOD	LOEWEN	SATIN NICKEL	CONTEMPORARY			EGRESS WINDOW
C4	3	304	BEDROOM 1	FIXED	2'-6" X 5'-0"	WOOD WINDOWS	ACCOYA	WOOD	WOOD	LOEWEN	SATIN NICKEL	CONTEMPORARY			TRANQUILITY GLASS
C5	3	304	BEDROOM 1	CASEMENT	2'-6" X 5'-0"	WOOD WINDOWS	ACCOYA	WOOD	WOOD	LOEWEN	SATIN NICKEL	CONTEMPORARY			TRANQUILITY GLASS
C6	3	303	BATH 2	OPERABLE TRANSOM	2'-3" X 5'-0"	ALUMINUM WINDOWS	450-T	CLEAR ANODIZED	CLEAR ANODIZED	FLEETWOOD	SATIN NICKEL/SILVER	CAM HANDLE			TRANSLUCENT GLASS
C7	3	301	STAIR HALL	FIXED FIRE RATED WINDOW	3'-1 3/8" X 8'-7" (X4 PANELS)	1-HR FIRE RATED ALUMINUM WINDOWS	SUPERLITE II XL-60 EXTERIOR	CLEAR ANODIZED	CLEAR ANODIZED	SAFTIFIRST					TRANSLUCENT GLASS 1-HR FIRE RATED. DEDUCT ALTERNATE WIRE GLASS
C8	3	307	MASTER BEDRM	CASEMENT	2'-6" X 5'-0"	ALUMINUM WINDOWS	450-T	CLEAR ANODIZED	CLEAR ANODIZED	FLEETWOOD	SATIN NICKEL/SILVER	CAM HANDLE			
C9	3	307	MASTER BEDRM	FIXED	2'-6" X 5'-0"	ALUMINUM WINDOWS	450-T	CLEAR ANODIZED	CLEAR ANODIZED	FLEETWOOD	SATIN NICKEL/SILVER	CAM HANDLE			EGRESS WINDOW
C10	3	307	MASTER BEDRM	CASEMENT	2'-6" X 5'-0"	ALUMINUM WINDOWS	450-T	CLEAR ANODIZED	CLEAR ANODIZED	FLEETWOOD	SATIN NICKEL/SILVER	CAM HANDLE			
C11	3	309	MASTER BATH	OPERABLE TRANSOM	2'-6" X 5'-0"	ALUMINUM WINDOWS	450-T	CLEAR ANODIZED	CLEAR ANODIZED	FLEETWOOD	SATIN NICKEL/SILVER	CAM HANDLE			
C12	3	309	MASTER BATH	OPERABLE TRANSOM	2'-6" X 5'-0"	ALUMINUM WINDOWS	450-T	CLEAR ANODIZED	CLEAR ANODIZED	FLEETWOOD	SATIN NICKEL/SILVER	CAM HANDLE			
C13	3	308	MASTER CLOSET	AWNING	3'-0" X 1'-6"	ALUMINUM WINDOWS	450-T	CLEAR ANODIZED	CLEAR ANODIZED	FLEETWOOD	SATIN NICKEL/SILVER	CAM HANDLE			
C14	3	306	LAUNDRY	AWNING	3'-0" X 1'-6"	ALUMINUM WINDOWS	450-T	CLEAR ANODIZED	CLEAR ANODIZED	FLEETWOOD	SATIN NICKEL/SILVER	CAM HANDLE			
D1	ROOF	301	STAIR HALL	LONGLIGHT F-OP-OP-F	13'-11 1/8" X 3'-10" VIF	CURB MOUNTED, SUN CONTROL FILM, NEAT® GLASS	CUSTOM CONFIG	WHITE	ALUM	VELUX	OPERABLE HUMIDITY SENNSIG				
D4	ROOF	303	BATH 2	ELECTRIC OPERATOR	3'-1 7/8" x 2'-6 1/16"	CURB MOUNTED, SUN CONTROL FILM, NEAT® GLASS	VSS-M04-2-0-04	WHITE	ALUM	VELUX	OPERABLE HUMIDITY SENNSIG				
D5	ROOF	309	MASTER BATH	FIXED	1'-8" X 6'-3"	CURB MOUNTED, SUN CONTROL FILM, NEAT® GLASS	FCM	WHITE	ALUM	VELUX	CUSTOM SIZE				

- NOTES:
- 1 ALL UNITS VIEWED FROM EXTERIOR.
 - 2 DIMENSIONS ARE WINDOW FRAME/DOOR SIZES. CONTRACTOR TO VIF & ALLOW FOR FRAME & SHIM SPACE AS REQ. NOTIFY THE ARCHITECT IF SPECIFIED WINDOW FRAME SIZE DOES NOT FIT AS SCHEDULED.
 - 3 ALL EXTERIOR GLAZING TO BE NFRC APPROVED. DUAL GLAZE LO-E .58 MAX U-FACTOR MIN.
 - 4 ALL GLAZING IN DOORS TO BE TEMPERED UON.
 - 5 VERIFY EXISTING OPENINGS ON SITE BEFORE ORDERING

WOOD WINDOWS

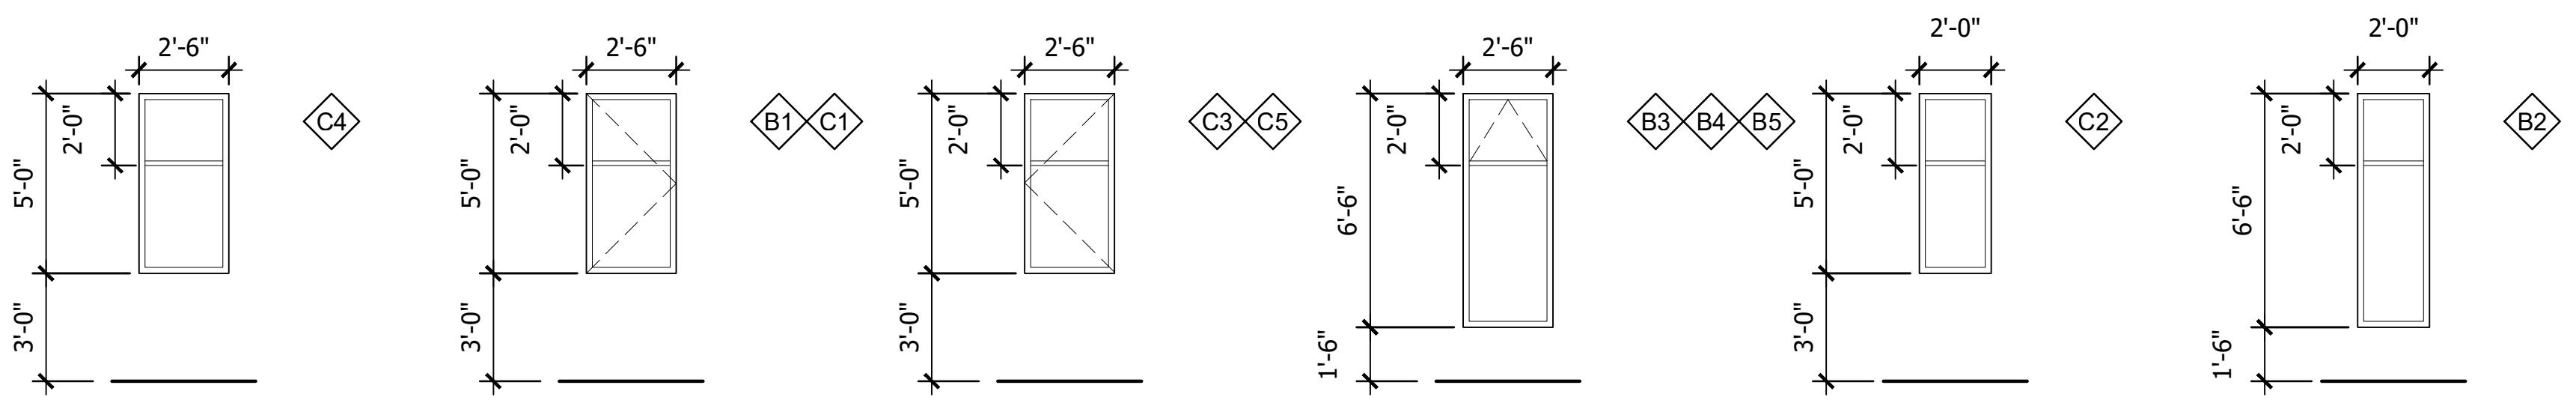

ALUMINUM WINDOWS

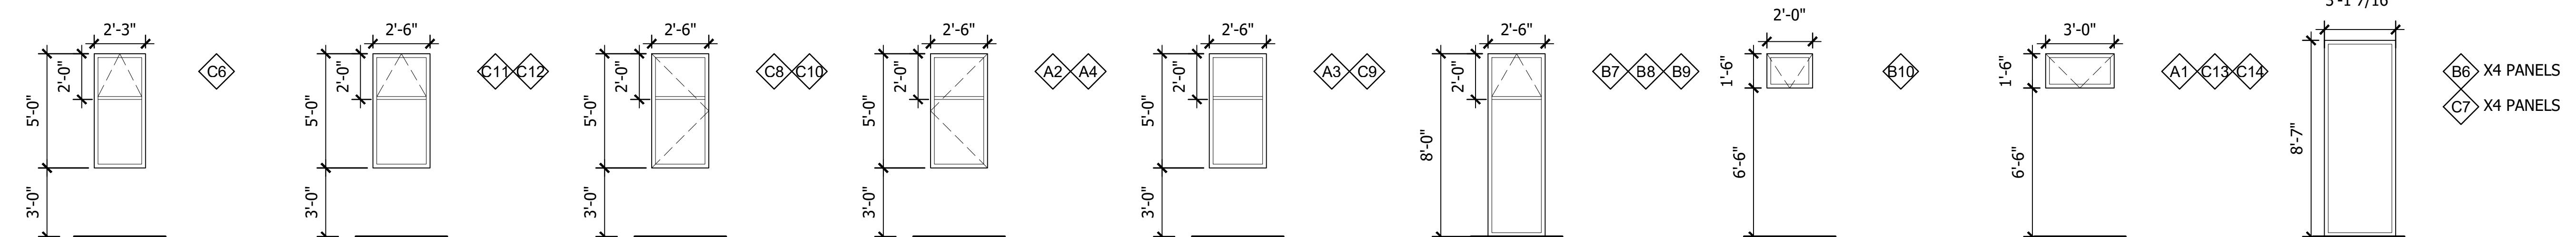

REVISIONS	DATE
PRE-APP	05.04.18
SITE PERMIT	05.11.18
DELTA 4	01.08.20
BUILDING PERMIT	02.11.20
STREET IMPRVTMT	02.27.20
CD SET	05.18.20

SCALE
1/4" = 1'-0"
SHEET TITLEWINDOW
SCHEDULE

SHEET NUMBER

A7.02

red dot studio

ARCHITECTURE AND DESIGN

Project: 830 BANBURY LANE WINDOWS AND SKYLIGHTS

CODE	LEVEL	RM#	ROOM NAME	OPERATION	SIZE WxH	DESCRIPTION	MODEL	FINISH		VENDOR	HARDWARE					NOTES
								INTERIOR	EXTERIOR		HARDWARE	HINGE	FINISH	HANDLE	ACCESSORY	
A1	1	102	HALL	FIXED - SEE PLAN	2'-0" X 7'-0"	ALUMINUM		ALUM	ALUM	FLEETWOOD	TBD	TBD	BRONZE	TBD		
A2	1	102	HALL	FIXED - SEE PLAN	5'-0" X 7'-0"	ALUMINUM		ALUM	ALUM	FLEETWOOD	TBD	TBD	BRONZE	TBD		TEMPERED GLASS
A3	1	103	POWDER	CASEMENT - SEE PLAN	3'-0" X 3'-6"	WOOD CLAD MARVIN ULTIMATE		PT-01	ALUM	MARVIN	TBD	TBD	BRONZE	TBD		
A4	1	108	JR SUITE	CASEMENT - SEE PLAN	3'-0" X 3'-6"	WOOD CLAD MARVIN ULTIMATE		PT-01	ALUM	MARVIN	TBD	TBD	BRONZE	TBD		
A5	1	108	JR SUITE	SLIDING - SEE PLAN	(2)3'-0" X 3'-6"	WOOD CLAD MARVIN ULTIMATE		PT-01	ALUM	MARVIN	TBD	TBD	BRONZE	TBD		
A6	1	108	JR SUITE	SLIDING - SEE PLAN	(2)3'-0" X 3'-6"	WOOD CLAD MARVIN ULTIMATE		PT-01	ALUM	MARVIN	TBD	TBD	BRONZE	TBD		
A7	1	109	JR BATH	CASEMENT - SEE PLAN	3'-0" X 3'-6"	WOOD CLAD MARVIN ULTIMATE		PT-01	ALUM	MARVIN	TBD	TBD	BRONZE	TBD		
A8	1	111	MUD ROOM	CASEMENT - SEE PLAN	3'-0" X 3'-6"	WOOD CLAD MARVIN ULTIMATE		PT-01	ALUM	MARVIN	TBD	TBD	BRONZE	TBD		
B1	2	201	MASTER BATH	CASEMENT - SEE PLAN	3'-0" X 3'-6"	WOOD CLAD MARVIN ULTIMATE		PT-01	ALUM	MARVIN	TBD	TBD	BRONZE	TBD		
B2	2	201	MASTER BATH	CASEMENT - SEE PLAN	3'-0" X 3'-6"	ALUMINUM		ALUM	ALUM	FLEETWOOD	TBD	TBD	BRONZE	TBD		TEMPERED GLASS
B3	2	205	HALL	FIXED	3'-0" X 3'-6"	WOOD CLAD MARVIN ULTIMATE		PT-01	ALUM	MARVIN	TBD	TBD	BRONZE	TBD		
B4	2	205	HALL	FIXED	3'-0" X 3'-6"	WOOD CLAD MARVIN ULTIMATE		PT-01	ALUM	MARVIN	TBD	TBD	BRONZE	TBD		
B5	2	205	HALL	FIXED	3'-0" X 3'-6"	WOOD CLAD MARVIN ULTIMATE		PT-01	ALUM	MARVIN	TBD	TBD	BRONZE	TBD		
B6	2	205	HALL	FIXED	3'-0" X 3'-6"	WOOD CLAD MARVIN ULTIMATE		PT-01	ALUM	MARVIN	TBD	TBD	BRONZE	TBD		
B7	2	205	HALL	FIXED	3'-0" X 3'-6"	WOOD CLAD MARVIN ULTIMATE		PT-01	ALUM	MARVIN	TBD	TBD	BRONZE	TBD		
B8	2	205	HALL	FIXED - SEE PLAN	(2)6'-6" X 6'-0"	WOOD CLAD MARVIN ULTIMATE		ALUM	ALUM	FLEETWOOD	TBD	TBD	BRONZE	TBD		
B9	2	206	BEDROOM 2	SLIDING - SEE PLAN	(2)3'-0" X 3'-6"	WOOD CLAD MARVIN ULTIMATE		PT-01	ALUM	MARVIN	TBD	TBD	BRONZE	TBD		
B10	2	204	BEDROOM 1	SLIDING - SEE PLAN	(2)3'-0" X 3'-6"	WOOD CLAD MARVIN ULTIMATE		PT-01	ALUM	MARVIN	TBD	TBD	BRONZE	TBD		
B11	2	203	MASTER BEDROOM	SLIDING - SEE PLAN	(2)3'-0" X 3'-6"	WOOD CLAD MARVIN ULTIMATE		PT-01	ALUM	MARVIN	TBD	TBD	BRONZE	TBD		
E1	ROOF	205	HALL	FIXED	1'-10-1/2" X 2'-10-1/2"	CURB MOUNT, SUN CONTROL FILM, NEAT GLASS	2234	PRE-FINISH WHITE		VELUX	TBD	TBD	BRONZE	TBD		
E2	ROOF	205	HALL	ELECTRIC	1'-10-1/2" X 2'-10-1/2"	CURB MOUNT, SUN CONTROL FILM, NEAT GLASS	2234	PRE-FINISH WHITE		VELUX	TBD	TBD	BRONZE	TBD		
E3	ROOF	205	HALL	FIXED	1'-10-1/2" X 2'-10-1/2"	CURB MOUNT, SUN CONTROL FILM, NEAT GLASS	2234	PRE-FINISH WHITE		VELUX	TBD	TBD	BRONZE	TBD		
E4	ROOF	205	HALL	ELECTRIC	1'-10-1/2" X 2'-10-1/2"	CURB MOUNT, SUN CONTROL FILM, NEAT GLASS	2234	PRE-FINISH WHITE		VELUX	TBD	TBD	BRONZE	TBD		
E5	ROOF	205	HALL	FIXED	1'-10-1/2" X 2'-10-1/2"	CURB MOUNT, SUN CONTROL FILM, NEAT GLASS	2234	PRE-FINISH WHITE		VELUX	TBD	TBD	BRONZE	TBD		
E6	ROOF	105	LIVING ROOM	FIXED	1'-10-1/2" X 2'-10-1/2"	CURB MOUNT, SUN CONTROL FILM, NEAT GLASS	2234	PRE-FINISH WHITE		VELUX	TBD	TBD	BRONZE	TBD		BLACK OUT BLINDS
E7	ROOF	105	LIVING ROOM	FIXED	1'-10-1/2" X 2'-10-1/2"	CURB MOUNT, SUN CONTROL FILM, NEAT GLASS	2234	PRE-FINISH WHITE		VELUX	TBD	TBD	BRONZE	TBD		BLACK OUT BLINDS
E8	ROOF	105	LIVING ROOM	FIXED	1'-10-1/2" X 2'-10-1/2"	CURB MOUNT, SUN CONTROL FILM, NEAT GLASS	2234	PRE-FINISH WHITE		VELUX	TBD	TBD	BRONZE	TBD		BLACK OUT BLINDS
E9	ROOF	105	LIVING ROOM	FIXED	1'-10-1/2" X 2'-10-1/2"	CURB MOUNT, SUN CONTROL FILM, NEAT GLASS	2234	PRE-FINISH WHITE		VELUX	TBD	TBD	BRONZE	TBD		BLACK OUT BLINDS
E10	ROOF	105	LIVING ROOM	FIXED	1'-10-1/2" X 2'-10-1/2"	CURB MOUNT, SUN CONTROL FILM, NEAT GLASS	2234	PRE-FINISH WHITE		VELUX	TBD	TBD	BRONZE	TBD		BLACK OUT BLINDS
E11	ROOF	202	BATH	ELECTRIC	1'-10-1/2" X 2'-10-1/2"	CURB MOUNT, SUN CONTROL FILM, NEAT GLASS	2234	PRE-FINISH WHITE		VELUX	TBD	TBD	BRONZE	TBD		

CODE	LEVEL	RM#	ROOM NAME	OPERATION	SIZE WxH	DESCRIPTION		FINISH		VENDOR	HARDWARE					NOTES
								INTERIOR	EXTERIOR		HARDWARE	HINGE	FINISH	HANDLE	HANDLE ACCESSORY	
101	1	102	HALL	INSWING - SEE PLAN	3'-0" X 7'-0"	SOLID CORE FLAT PANEL		PLANK CEDAR	PLANK CEDAR	TBD	LOCKING	BRONZE	BRONZE	TBD		
102	1	102	HALL	INSWING - SEE PLAN	2'-4" X 7'-0"	SOLID CORE		STAIN GRADE OAK	STAIN GRADE OAK	TBD	PASSAGE	BRONZE	BRONZE	TBD		
103	1	103	POWDER	INSWING - SEE PLAN	2'-4" X 7'-0"	SOLID CORE		STAIN GRADE OAK	STAIN GRADE OAK	TBD	PRIVACY	BRONZE	BRONZE	TBD		
104	1	105	LIVING ROOM	SLIDING - SEE PLAN	19'-0" X 7'-0"	ALUMINUM GLASS	SERIES 3070	ALUMINUM	ALUMINUM	FLEETWOOD	LOCKING	BRONZE	BRONZE	TBD	2 FIXED, 2 SLIDER	
105	1	107	BEDROOM	POCKET SLIDING	(2)3'-0" X 7'-0"	WOOD GLASS		STAIN GRADE OAK	STAIN GRADE OAK	TBD	PRIVACY	BRONZE	BRONZE	TBD		
106	1	107	BEDROOM	SLIDER	(2)3'-0" X 7'-0"	WOOD CLAD GLASS		STAIN GRADE OAK	WOOD CLAD	MARVIN	LOCKING	BRONZE	BRONZE	TBD		
107	1	108	JR SUITE	INSWING - SEE PLAN	3'-0" X 7'-0"	SOLID CORE		STAIN GRADE OAK	STAIN GRADE OAK	TBD	PRIVACY	BRONZE	BRONZE	TBD		
108	1	106	KITCHEN	OUTSWING - SEE PLAN	2'-4" X 7'-0"	SOLID CORE		STAIN GRADE OAK	STAIN GRADE OAK	TBD	PASSAGE	BRONZE	BRONZE	TBD		
109	1	109	JR SUITE	INSWING - SEE PLAN	(2)3'-0" X 7'-0"	SOLID CORE		STAIN GRADE OAK	STAIN GRADE OAK	TBD	PASSAGE	BRONZE	BRONZE	TBD		
110	1	108	JR SUITE	INSWING - SEE PLAN	(2)2'-0" X 7'-0"	SOLID CORE		STAIN GRADE OAK	STAIN GRADE OAK	TBD	PASSAGE	BRONZE	BRONZE	TBD		
111	1	109	JR BATH	POCKET SLIDING	2'-4" X 7'-0"	SOLID CORE		STAIN GRADE OAK	STAIN GRADE OAK	TBD	PRIVACY	BRONZE	BRONZE	TBD		
112	1	111	MUD ROOM	INSWING - SEE PLAN	3'-0" X 7'-0"	SOLID CORE		STAIN GRADE OAK	STAIN GRADE OAK	TBD	PASSAGE	BRONZE	BRONZE	TBD		
114	1	111	MUD ROOM	INSWING - SEE PLAN	3'-0" X 7'-0"	SOLID CORE		STAIN GRADE OAK	STAIN GRADE OAK	TBD	PASSAGE	BRONZE	BRONZE	TBD		
115	1	101	GARAGE		16'-0" X 8'-6" (V.I.F)	SOLID CORE		PLANK CEDAR	PLANK CEDAR	TBD	LOCKING	BRONZE	BRONZE	TBD	20 MIN RATED DOOR	
201	2	201	MASTER BATH	POCKET SLIDING	2'-6" X 7'-2"</											